
Polițe din beton decorativ și stejar pentru viniluri


2 polițe din microciment pe placaj, 80 × 33 × 4 cm, în dreapta televizorului, la 127,8 și 171,2 cm, prinse ascuns în perete, și o verticală din stejar lipită de cea de jos · A: beton gri și stejar; B: beton antracit și stejar (planul e comun)

cote în cm · scara 1:15 (A3), detalii 1:5 · cotele cu „~” sunt din fotografie, de verificat


VEDERE FRONTALĂ (1:15)

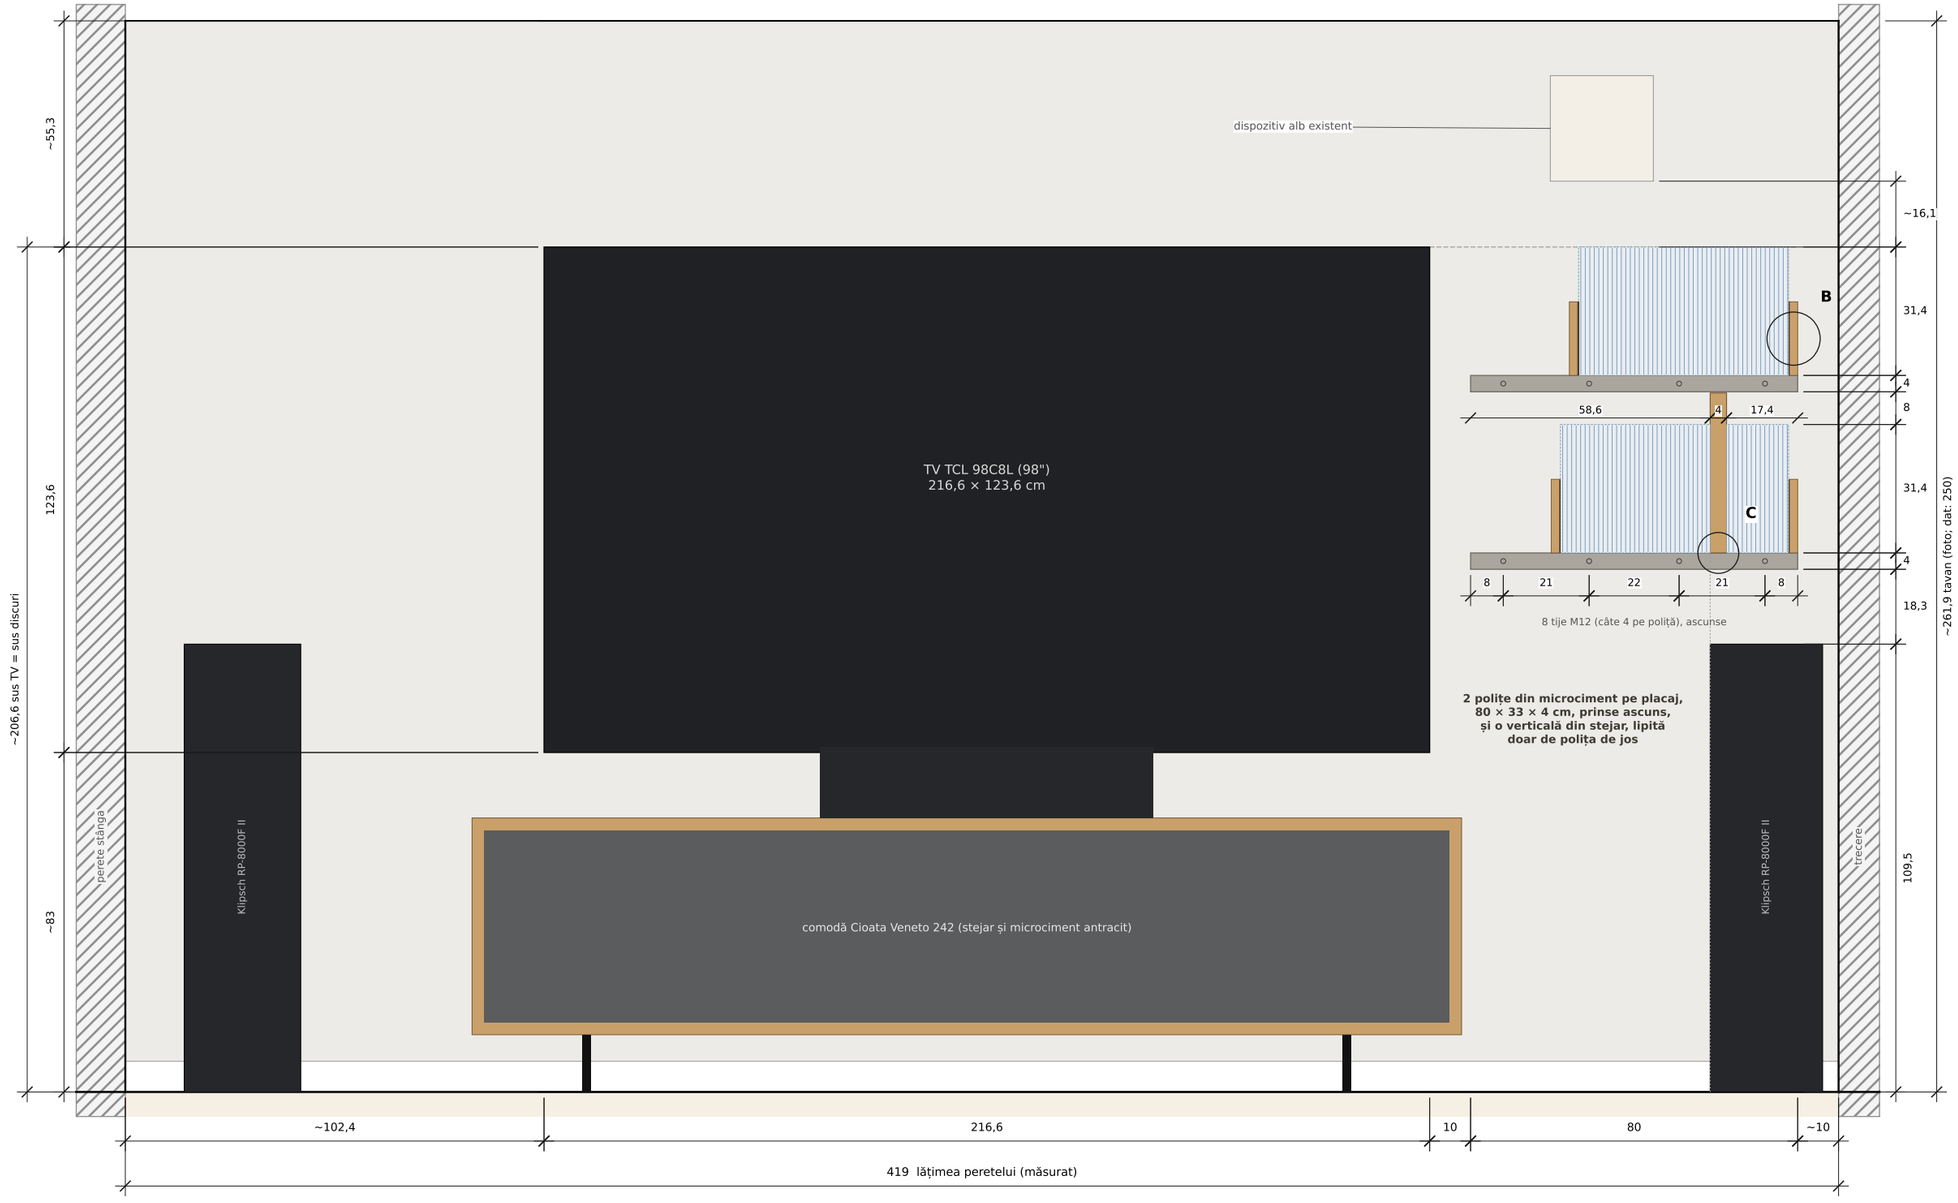


SECȚIUNE PRIN VERTICALĂ (1:15)

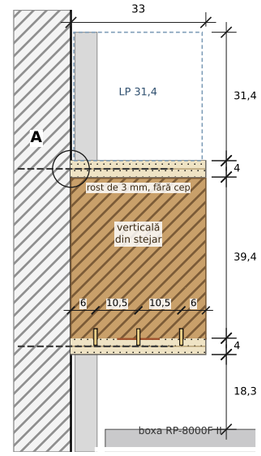

DETALIU C – verticala (1:5)

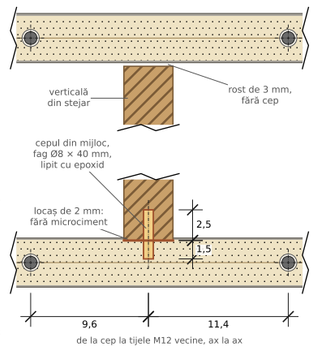


DETALIU A – tija (1:5)

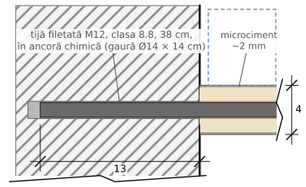

tija intră 25 cm în poliță, în canalul Ø14 × 26 cm făcut din două semicanale frezate înainte de lipire; adeziv epoxidic doar pe ultimii ~8 cm, lângă perete

DETALIU B – opritor (1:5)

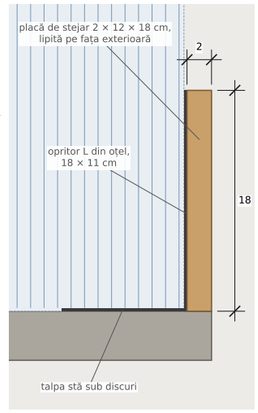

LEGENDĂ

- microciment ~2 mm (A: beton gri; B: antracit)
- miez: 2 plăci de placaj de mesteacăn, 18 mm
- stejar masiv: verticala, plăcile opritoarelor
- cep din fag, lipit cu adeziv epoxidic
- oțel: tije M12 de clasa 8.8, opritoare L

MATERIALE ȘI EXECUȚIE

1. 2 polițe de 80 × 33 × 4 cm (~8,5 kg una): miez din 2 plăci de placaj de mesteacăn de 18 mm, lipite; ~2 mm de microciment, cu muchii R3, plasă și lac PU mat. Spatele și canalele se sigilează.
2. Canalele tijelor, Ø14 × 26 cm, la 8, 29, 51 și 72 cm de capătul din stânga: din semicanale frezate în plăcile miezului înainte de lipire (detaliul A).
3. Verticala, din stejar masiv, 4 × 33 × 39,3 cm (~3,7 kg), cu fibra pe verticală: stă în locașul de 2 mm al poliței de jos și se oprește la 3 mm sub cea de sus (detaliul C).
4. 3 cepuri din fag Ø8 × 40 mm, la 6, 16,5 și 27 cm de perete, intră 1,5 cm în poliță și 2,5 cm în verticală. Doar cel din mijloc e lipit, cu adeziv epoxidic pe ~10 cm; celelalte două stau în găuri ovale de 8 × 11 mm.
5. 8 tije M12 de clasa 8.8, de 38 cm: 13 cm în ancoră chimică (găuri Ø14 × 14 cm), 25 cm în poliță.
6. 4 opritoare L din oțel, de 18 × 11 cm, îmbrăcate în stejar, cu folie sub talpă (detaliul B).
7. Șablonul: 80 × 20 × 4 cm, din același miez, cu canalele la 2 cm de fața de jos.

DE CE AȘA

- Beton la orizontale, stejar la verticală, ca la comodă; verticala urcă din marginea boxei.
- Pe placaj, polița are ~8,5 kg; din beton GFRC masiv, ar avea ~22 kg.
- Plină, polița de jos are ~41,2 kg, iar cea de sus ~39,3 kg (ticsite: ~52,7 și ~51,3 kg). Încap ~126 de discuri jos și ~134 sus (ticsite, ~362).
- Poliță de jos ticsită, doar în tije: ~227 MPa, rezervă ~2,8 la clasa 8.8; la 4.8, doar ~1,4, deci nu se folosește.
- Sprijinită pe perete, poliță trage de fiecare ancoră cu ~1,07 kN: fișa ancorei și proba confirmă că peretele o ține.
- Cepurile stau la 9,6 și 11,4 cm de tijele vecine, ax la ax: nu ating canalele.

MONTAJUL

1) Tijele de jos, prin șablon, în ancora chimică; șablonul stă la nivel până se întărește ancora.
2) Adeziv epoxidic pe ultimii ~8 cm ai tijelor; polița de jos, cu verticala (~12,2 kg), până la perete.
3) Șablonul, pe verticală, peste distanțiere de 3 mm: tijele de sus, apoi polița de sus (~8,5 kg).
4) Proba: 55 kg pe fiecare poliță, 24 de ore. Dacă polițele rămân la nivel și rostul de 3 mm e liber, urmează opritoarele și discurile.

COTE

Găurile se măsoară de la televizor, nu de la tavan: la 18, 39, 61 și 82 cm de marginea lui din dreapta și la 33,4 și 76,8 cm sub cea de sus.

COTE DE MĂSURAT

a) înălțimea camerei (poza dă ~262, nu 250);
b) marginile televizorului: cea de sus, de la pardoseală, și cea din dreapta, de la colț;
c) marginea din stânga a boxei din dreapta, de la colț (~387,6): locul verticalei;
d) din ce e peretele și cât e de gros: de el depind ancora și manșoanele-sită;
e) codul de finisaj al comodei (CS, NO, FE sau SO), pentru stejar;
f) dacă trecerea din dreapta are ușă care se deschide spre perete (poliță e la 10 cm);
g) cablurile din perete, cu detectorul, mai ales sub dispozitivul alb.

PLAN – VEDERE DE SUS (1:15)

